

BOČNÝ POHĽAD M 1:30



Sklon je parametrický (max. 55°) – pri inej hodnote spustiť generuj.py --uhol XX, výkres a kusovník sa prepočítajú

ROZBEHOVÁ RAMPA (ROLL-IN) NA KONTAINERI - OCEĽOVÁ KONŠTRUKCIA


Bočný pohľad - hlavné rozmery

List 1/4

lakel 50x50x3 – S235 | výška plošiny 4200 | sklon 55° | rozmery v mm

Dátum: 01.10.2026

BOČNICA RAMPY - ŠABLÓNA (2 ks, zrkadlovo rovnaké) M 1:30

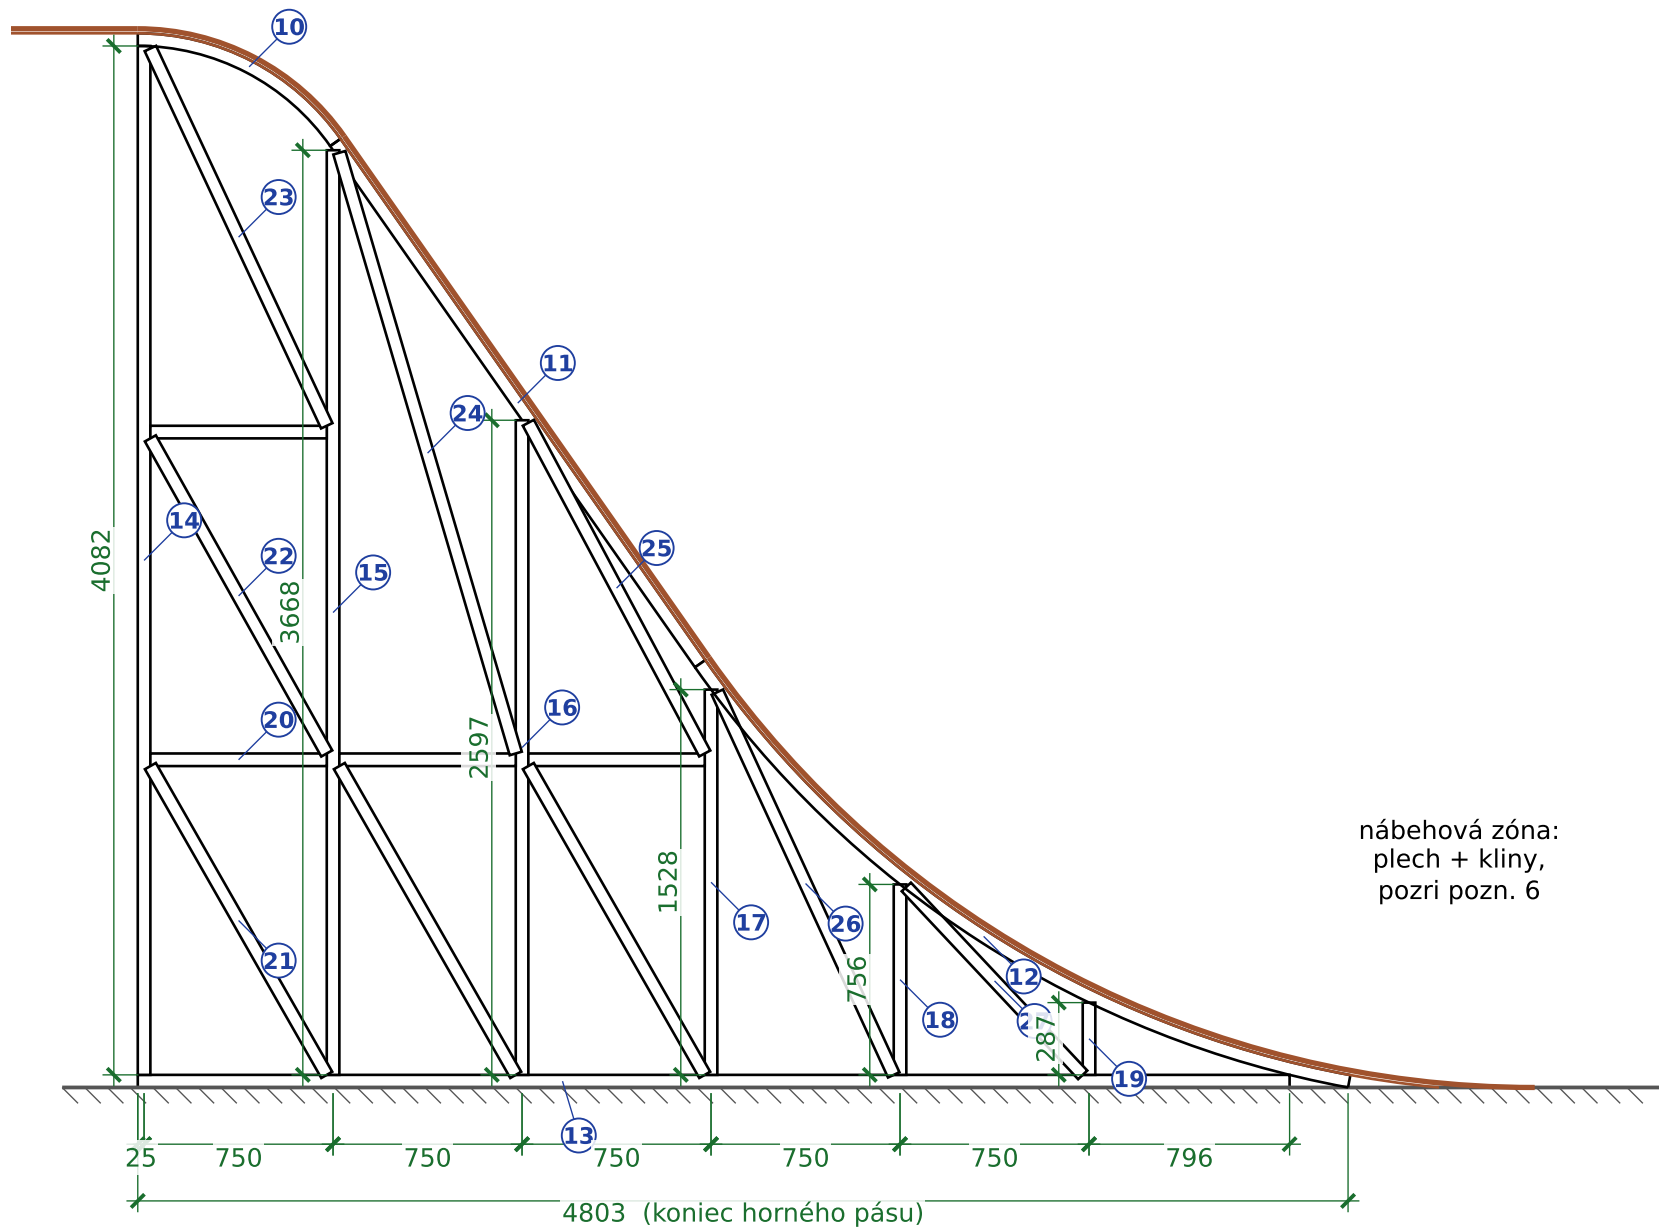

stĺpik	x osi [mm]	dĺžka [mm]	horný rez
S1	25	4082	1.5°
S2	775	3668	55.0°
S3	1525	2597	55.0°
S4	2275	1528	53.5°
S5	3025	756	38.3°
S6	3775	287	25.8°

Postup: bočnicu vyznačiť 1:1 na rovnej podlahe (DXF), zvariť obe bočnice na sebe, potom spojiť priečkami (poz. 28, 32, 36) a diagonálami. Dĺžky diagonál zakrátiť na mieru.

ROZBEHOVÁ RAMPA (ROLL-IN) NA KONTAJNERI - OCEĽOVÁ KONŠTRUKCIA


Bočnica rampy - šablóna, pozície

List 2/4


Jakel 50x50x3 - S235 | výška plošiny 4200 | sklon 55° | rozmery v mm

Dátum: 01.10.2026


POHLÁD ZHORA (bez preglejky) M 1:40

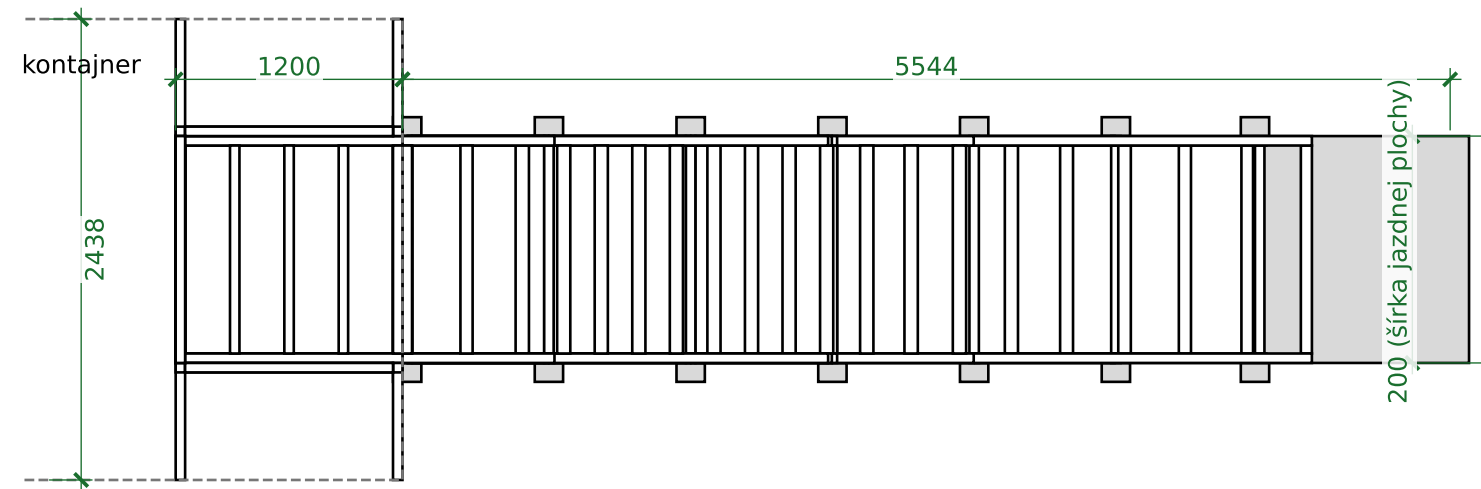

POHLÁD ZOZADU (od plošiny) M 1:40

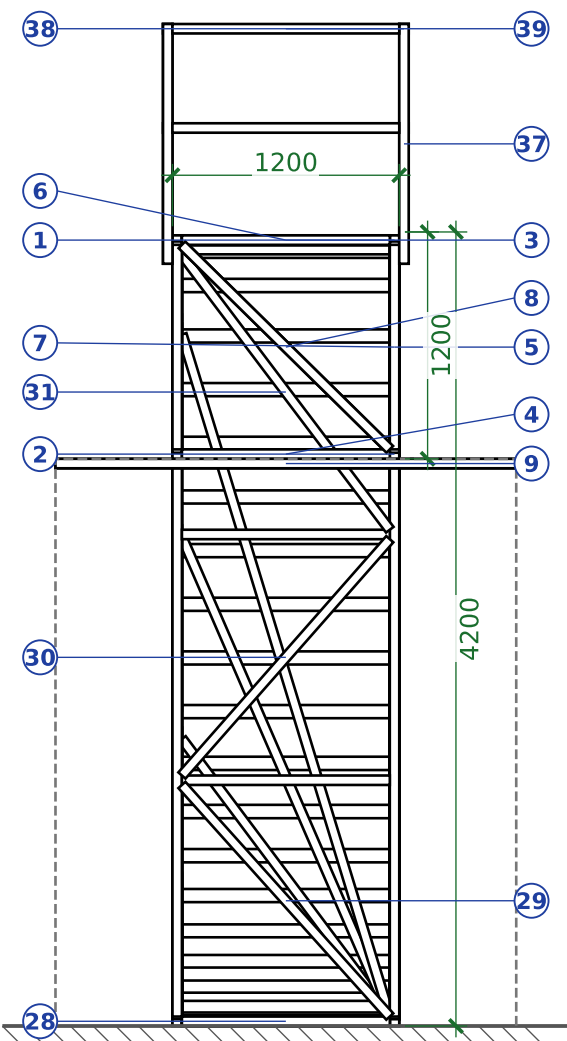

IZOMETRIA

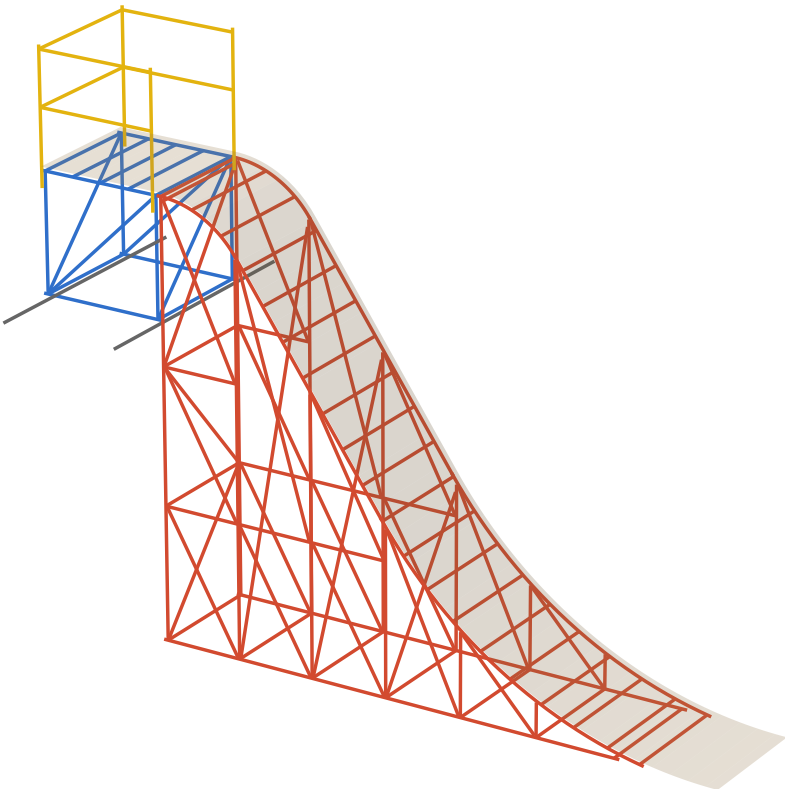

modrá A – plošina | červená B – rampa | žltá C – zábradlie | sivá D – podpery

ROZBEHOVÁ RAMPA (ROLL-IN) NA KONTAJNERI - OCEĽOVÁ KONŠTRUKCIA

Pohľad zhora, zozadu, izometria

List 3/4

Jakel 50x50x3 – S235 | výška plošiny 4200 | sklon 55° | rozmery v mm

Dátum: 01.10.2026

poz.	skup.	názov	profil / rozmer	dĺžka v osi [mm]	ks	spolu [m]	kg	poznámka
1	A	Plošina - horný rám pozdĺžny	jakel 50x50x3	1200	2	2.40	10.2	
2	A	Plošina - spodný rám pozdĺžny	jakel 50x50x3	1200	2	2.40	10.2	
3	A	Plošina - horný rám priečny	jakel 50x50x3	1100	2	2.20	9.4	
4	A	Plošina - spodný rám priečny	jakel 50x50x3	1100	2	2.20	9.4	
5	A	Plošina - stĺpik	jakel 50x50x3	1082	4	4.33	18.4	
6	A	Plošina - priečnik pod preglejku	jakel 50x50x3	1100	3	3.30	14.0	
7	A	Plošina - diagonála bočná	jakel 50x50x3	1543	2	3.09	13.1	zakrátiť na mieru
8	A	Plošina - diagonála čelná	jakel 50x50x3	1543	2	3.09	13.1	zakrátiť na mieru
9	D	Podperný nosník cez kontajner	jakel 50x50x3	2438	2	4.88	20.7	ukladať na horné pozdĺžniky kontajnera; odporúčané 100x50x4
10	B	Horný pás - horný oblúk (zakružiť)	jakel 50x50x3	919	2	1.84	7.8	zakružiť v osi R957
11	B	Horný pás - rovný úsek	jakel 50x50x3	2524	2	5.05	21.5	konce kolmo, sklon 55°
12	B	Horný pás - spodný plynulý oblúk (zakružiť)	jakel 50x50x3	3141	2	6.28	26.7	zakružiť v osi R4043
13	B	Spodný pás (na teréne)	jakel 50x50x3	4571	2	9.14	38.9	koniec zrezať pod horný pás
14	B	Bočnica - stĺpik	jakel 50x50x3	4082	2	8.16	34.7	hore rez 1.5° (podľa pásu)
15	B	Bočnica - stĺpik	jakel 50x50x3	3668	2	7.34	31.2	hore rez 55.0° (podľa pásu)
16	B	Bočnica - stĺpik	jakel 50x50x3	2597	2	5.19	22.1	hore rez 55.0° (podľa pásu)
17	B	Bočnica - stĺpik	jakel 50x50x3	1528	2	3.06	13.0	hore rez 53.5° (podľa pásu)
18	B	Bočnica - stĺpik	jakel 50x50x3	756	2	1.51	6.4	hore rez 38.3° (podľa pásu)
19	B	Bočnica - stĺpik	jakel 50x50x3	287	2	0.57	2.4	hore rez 25.8° (podľa pásu)
20	B	Bočnica - pažďík	jakel 50x50x3	700	8	5.60	23.8	
21	B	Bočnica - diagonála	jakel 50x50x3	1411	6	8.47	36.0	zakrátiť na mieru (šablóna 1:1)
22	B	Bočnica - diagonála	jakel 50x50x3	1433	2	2.87	12.2	zakrátiť na mieru (šablóna 1:1)
23	B	Bočnica - diagonála	jakel 50x50x3	1652	2	3.30	14.0	zakrátiť na mieru (šablóna 1:1)
24	B	Bočnica - diagonála	jakel 50x50x3	2484	2	4.97	21.1	zakrátiť na mieru (šablóna 1:1)
25	B	Bočnica - diagonála	jakel 50x50x3	1487	2	2.97	12.6	zakrátiť na mieru (šablóna 1:1)
26	B	Bočnica - diagonála	jakel 50x50x3	1672	2	3.34	14.2	zakrátiť na mieru (šablóna 1:1)
27	B	Bočnica - diagonála	jakel 50x50x3	1023	2	2.05	8.7	zakrátiť na mieru (šablóna 1:1)
28	B	Zadná stena - priečka	jakel 50x50x3	1100	4	4.40	18.7	
29	B	Zadná stena - diagonála	jakel 50x50x3	1646	1	1.65	7.0	zakrátiť na mieru
30	B	Zadná stena - diagonála	jakel 50x50x3	1665	1	1.67	7.1	zakrátiť na mieru
31	B	Zadná stena - diagonála	jakel 50x50x3	1825	1	1.83	7.8	zakrátiť na mieru
32	B	Spodná priečka	jakel 50x50x3	1100	6	6.60	28.0	
33	B	Priečna diagonála	jakel 50x50x3	3772	1	3.77	16.0	zakrátiť na mieru
34	B	Priečna diagonála	jakel 50x50x3	2765	1	2.77	11.8	zakrátiť na mieru
35	B	Priečna diagonála	jakel 50x50x3	1835	1	1.83	7.8	zakrátiť na mieru
36	B	Priečnik pod preglejku	jakel 50x50x3	1100	20	22.00	93.5	
37	C	Zábradlie - stĺpik	jakel 50x50x3	1268	4	5.07	21.6	privariť z boku na horný rám plošiny
38	C	Zábradlie - madlo/medzimaklo bočné	jakel 50x50x3	1100	4	4.40	18.7	
39	C	Zábradlie - madlo/medzimaklo zadné	jakel 50x50x3	1200	2	2.40	10.2	
40	B	Kotviaca pätká 150x100x8	plech 8 mm 150x100	-	14	-	13.2	2x otvor Ø14, kotva M12 do betónu
41	B	Nábehový podkladný plech	plech 5 mm 1123x1200	-	1	-	52.9	na betón, k nemu privariť koniec pásov
		SPOLU				168.0 m	780 kg	+ 10 % na prerezy / odpad

TECHNICKÉ POZNÁMKY

- Materiál: jakel 50x50x3 (EN 10219, S235JRH), plechy S235. Zvary kútové a=3 mm, obvodové, súvislé.
- Horný pás: poz. 10 zakružiť na polomer v osi R957, poz. 12 na R4043 (zakružovačka profilov). Pás musí byť plynulý – spoje na tupo, prebrúsiť zarovno.
- Priečniky pod preglejku (poz. 36) vrchom zarovno s horným pásom, rozostup max. 350 mm po oblúku.
- Preglejka 18 mm protišmyková; v rádiusoch skladať z tenších vrstiev (spodný R: 2x9 mm, horný R: 3x6 mm). Skrutky do jaklu samorezné.
- Plošina (A) a rampa (B) sa zvárajú samostatne, na mieste spojiť M12 skrutkami cez susedné stĺpiky (x = 0). Zábradlie (C) privariť na horný rám.
- Nábeh: horný pás končí tam, kde jeho spodná hrana dosadne na terén; posledný úsek do nuly riešiť podkladným plechom (poz. 41) a drevenými klinmi + nábehový plech 3 mm.
- Kotvenie: rampa na betónové pätky/pás (terén je hlina!), pätky M12; plošina kotvíť ku kontajneru cez rohové prvky (twistlock / zvarené príložky) – NIE na tenký plech strechy.
- Podperné nosníky (D) ukladať na horné pozdĺžniky kontajnera, poloha plošiny podľa skutočnosti. Odporúčaný silnejší profil 100x50x4.
- Povrchová úprava: odmasťiť, základná farba + vrchná (alebo žiarový zinok). Ostré hrany zabrusiť.
- Konštrukcia vo výške 4,2 m pre verejnosť – pred výrobou nechať overiť statikom (zaťaženie, vietor, kotvenie). Výkres je pracovný podklad.

ROZBEHOVÁ RAMPA (ROLL-IN) NA KONTAJNERI - OCEĽOVÁ KONŠTRUKCIA

Kusovník a technické poznámky	List 4/4
Jakel 50x50x3 – S235 výška plošiny 4200 sklon 55° rozmery v mm	Dátum: 01.10.2026